


Building C/D - 3 Bedroom

Detailed three-bedroom plan with bedrooms, baths, closets, stairs, and room dimensions

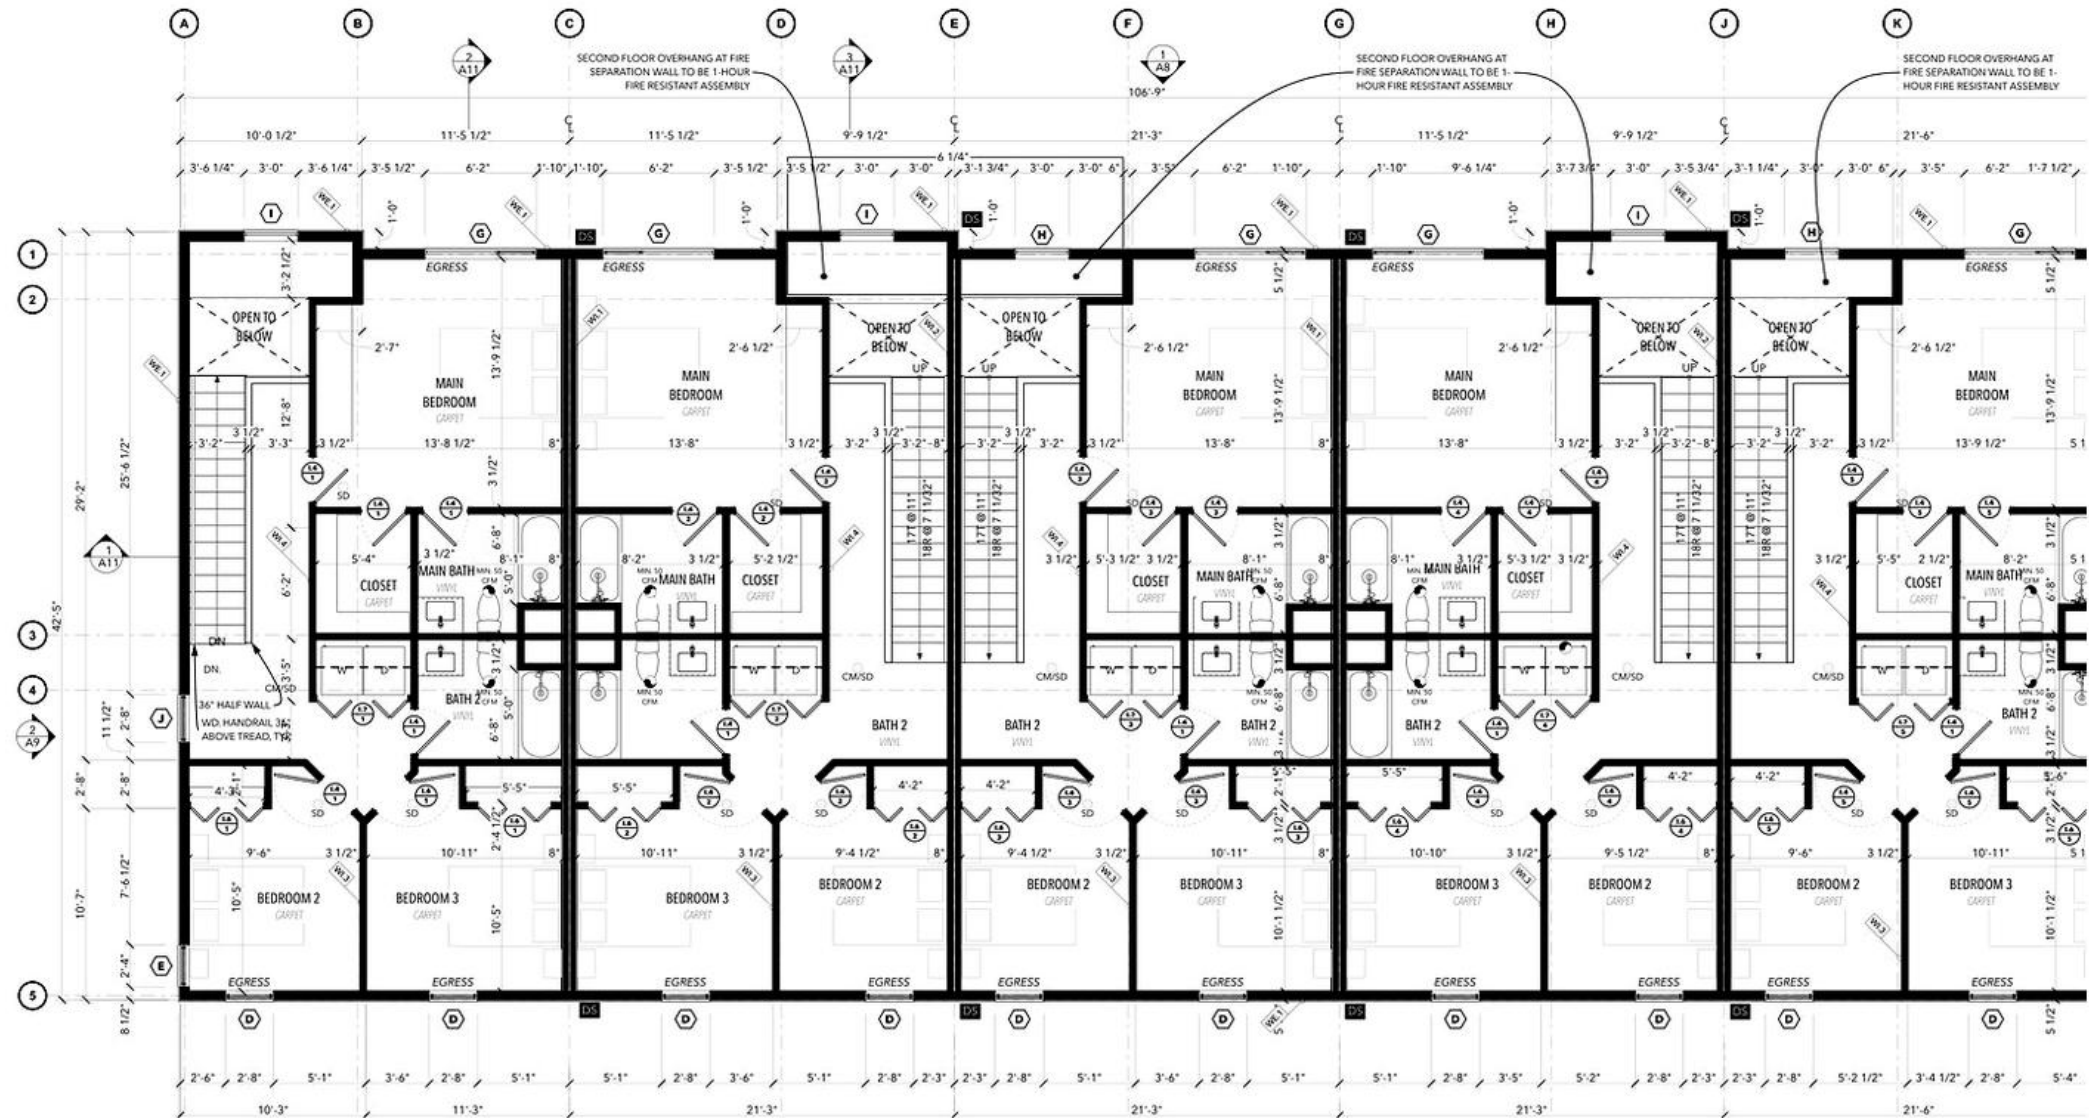

SECOND FLOOR
SCALE: 1/4" = 1'-0"

SYMBOL KEY

EXTERIOR DOOR ID	FINISH ID	SMOKE DETECTOR (MOUNT ON CEILING)	HEAT DETECTOR (TO BE INTERCONNECTED WITH UNIT SMOKE ALARMS PER R314.2.1 & R314.2.3)
INTERIOR DOOR ID	EGRESS OPENING	SMOKE DETECTOR (MOUNT ON WALL)	HOSE BIB
WINDOW ID	EXHAUST VENT	COMBO SMOKE/CARBON MONOXIDE DETECTOR (MOUNT ON CEILING)	TEMPERED GLAZING (ELEVATION)
SKYLIGHT ID	EXHAUST VENT W/ LIGHT	COMBO SMOKE/CARBON MONOXIDE DETECTOR (MOUNT ON WALL)	
WALL ID			