


Building C/D - First Floor

Detailed building layout with unit labels, kitchens, living areas, baths, and patios

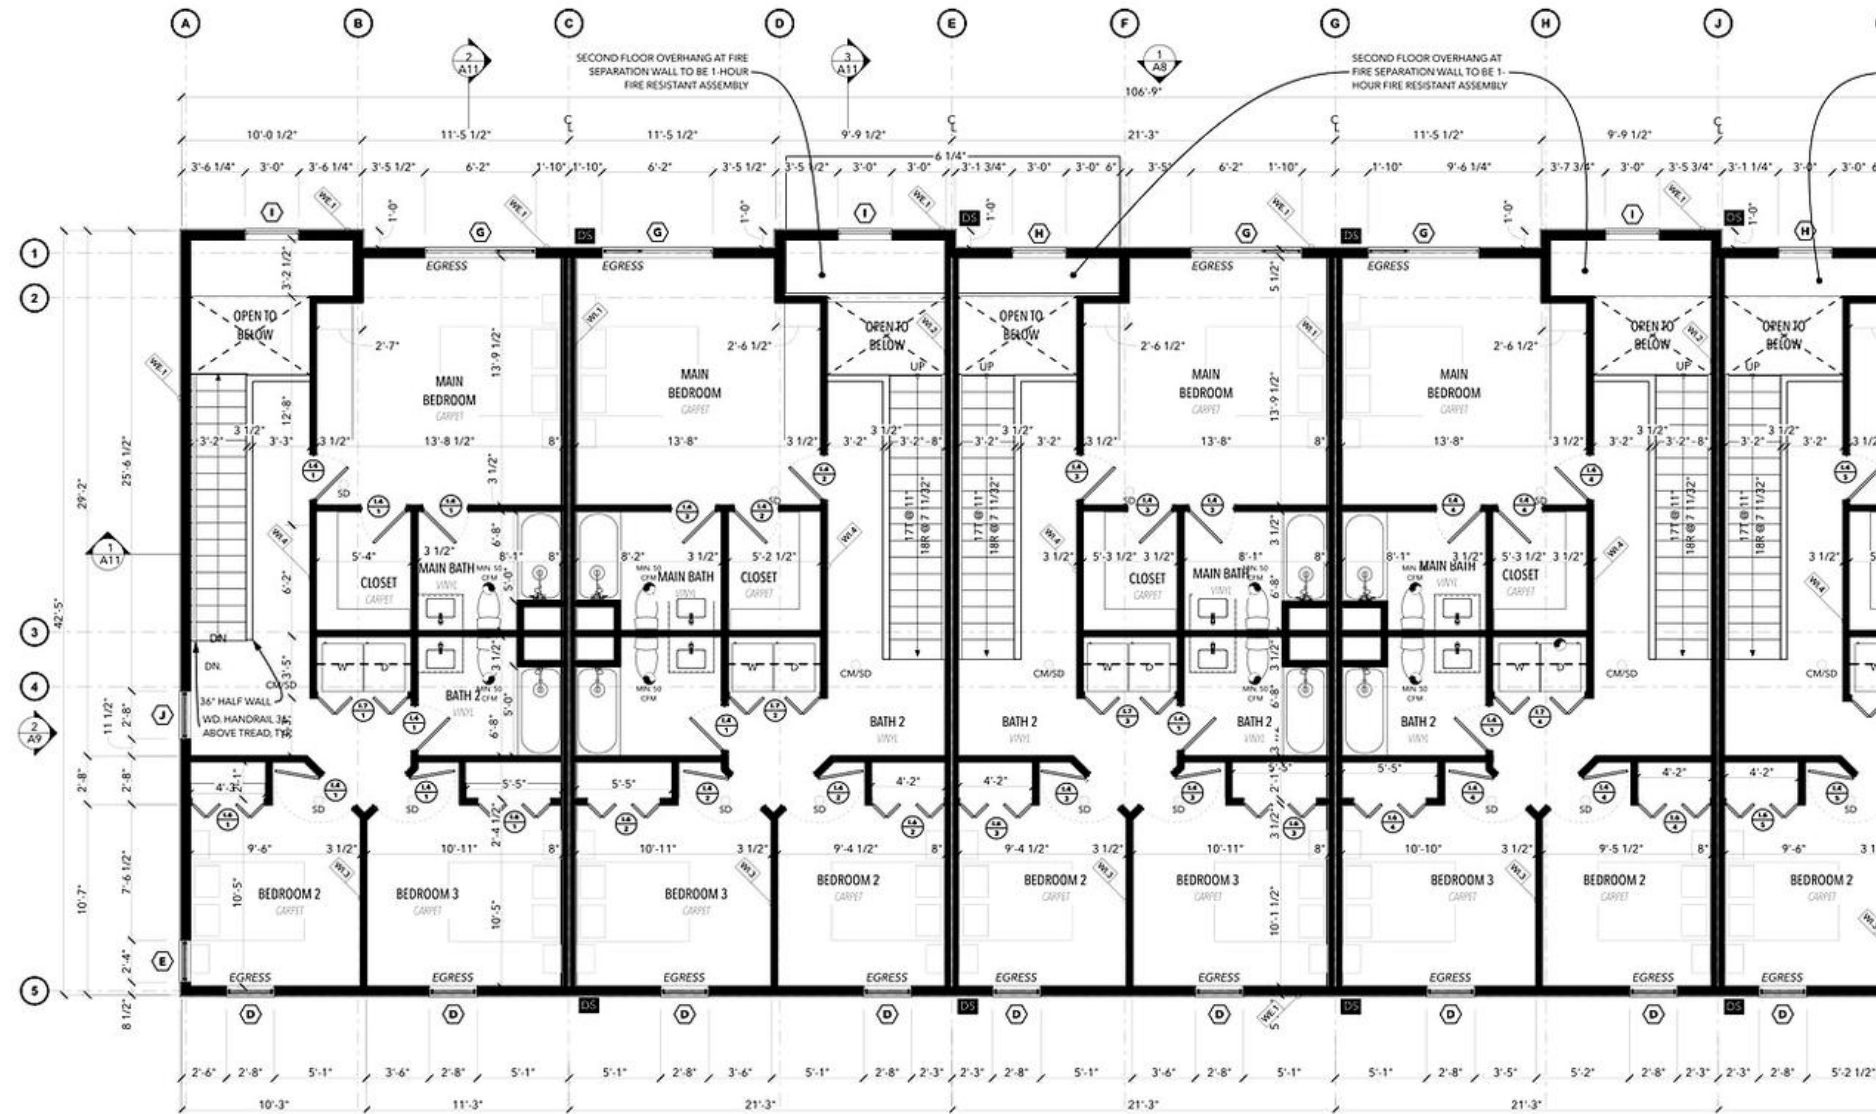

SECOND FLOOR

SCALE: 1/4" = 1'-0"

SYMBOL KEY

	EXTERIOR DOOR ID		FINISH ID		SMD ○ SMOKE DETECTOR (MOUNT ON CEILING)		HD ○ HEAT DETECTOR (TO BE INTERCONNECTED WITH UNIT SMOKE ALARMS PER R314.2.1 & R314.2.3)
	INTERIOR DOOR ID		EGRESS		SMD ⊥ SMOKE DETECTOR (MOUNT ON WALL)		HOSE BIB
	WINDOW ID		EXHAUST VENT		SCD ○ COMBO SMOKE/CARBON MONOXIDE DETECTOR (MOUNT ON CEILING)		TEMPERED GLAZING (ELEVATION)
	SKYLIGHT ID		EXHAUST VENT W/ LIGHT		SCD ⊥ COMBO SMOKE/CARBON MONOXIDE DETECTOR (MOUNT ON WALL)		
	WALL ID						